
様式第９


整理番号	1	図面番号	1

所在地	東京都練馬区南大泉〇丁目〇番
所有者住所	東京都練馬区南大泉〇丁目〇番〇〇号
所有者	国土　二郎

構造概要	
構造	木造２階建
用途	専用住宅
基礎	布コンクリート
屋根	日本瓦葺
外壁	色モルタル塗り

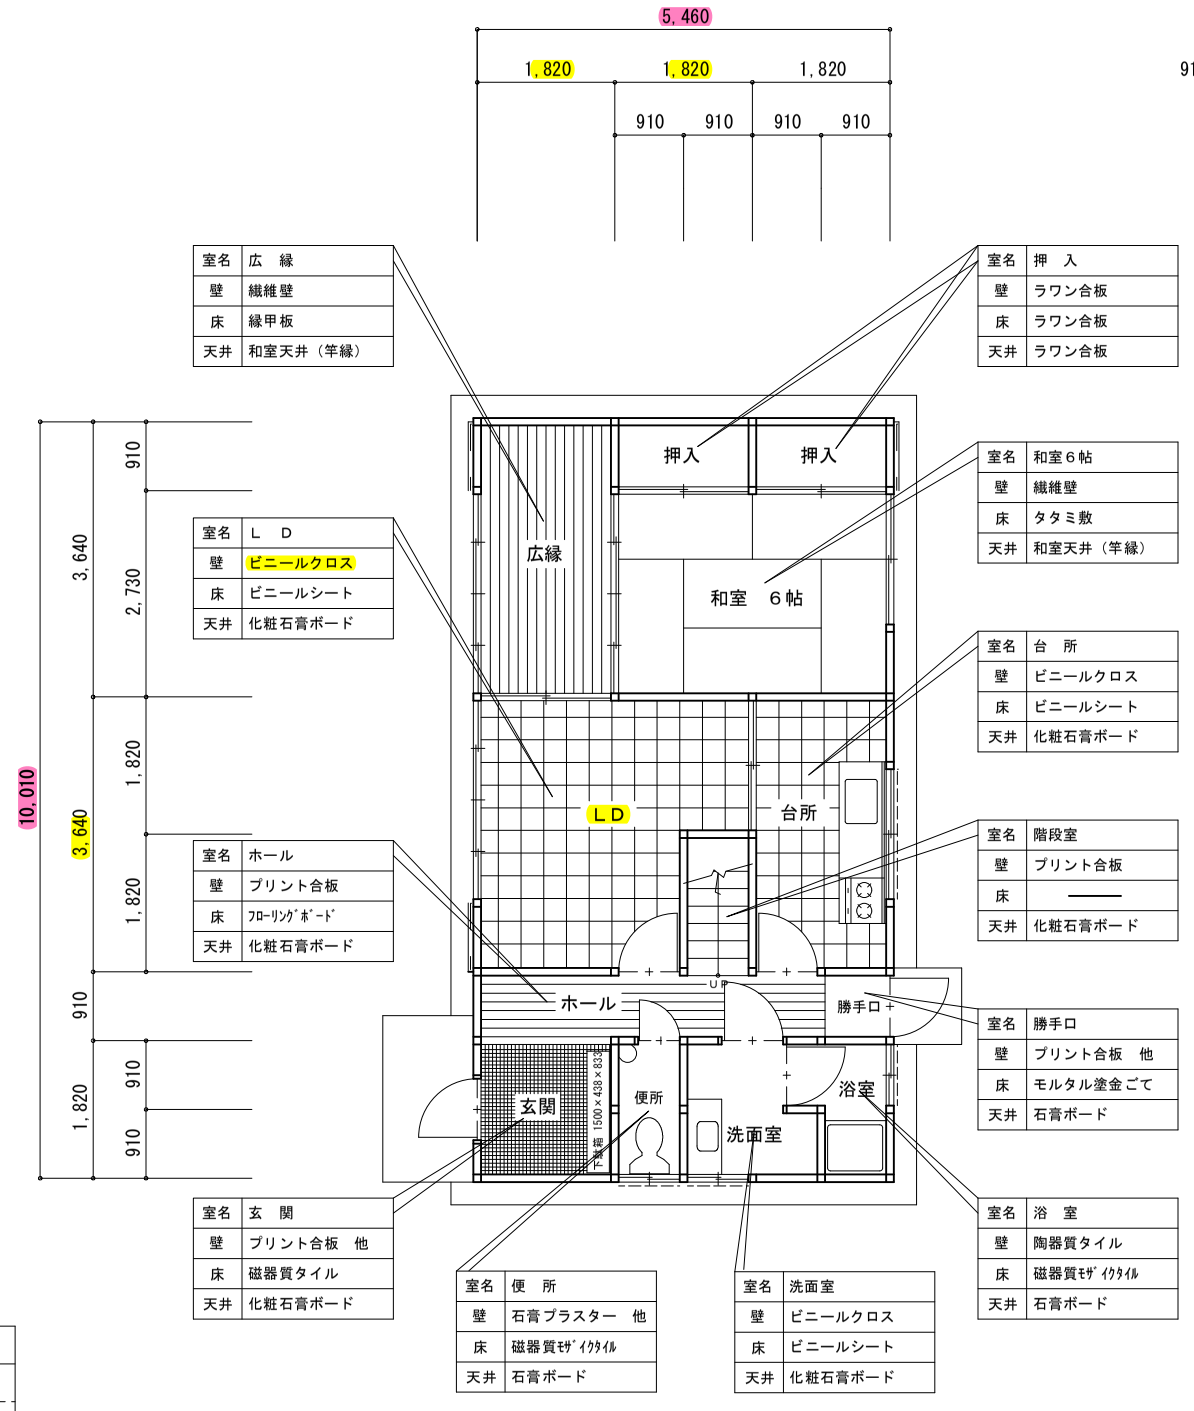

１階　平面図

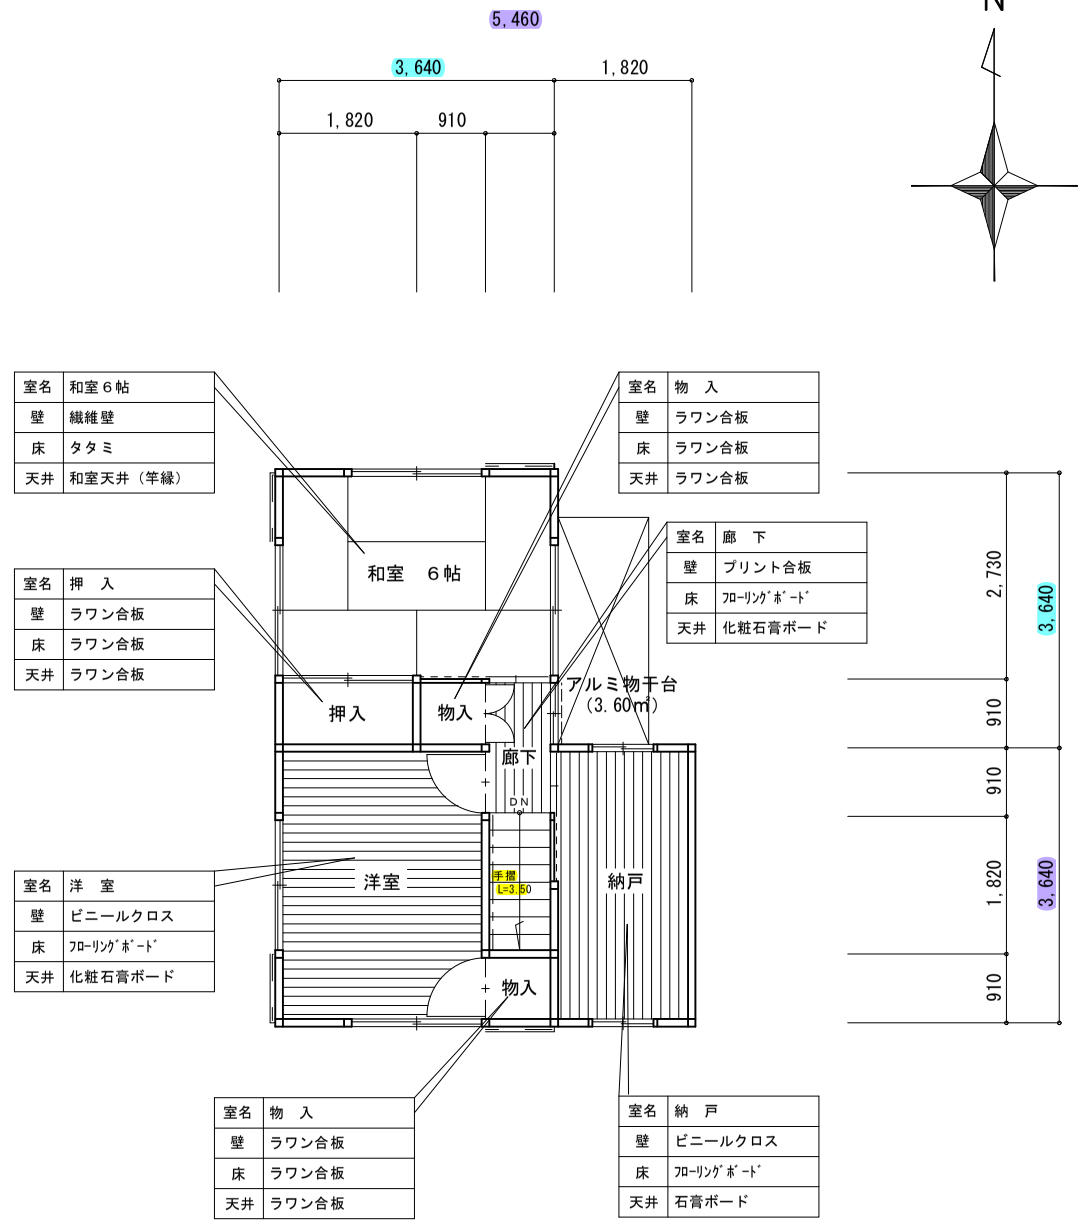

２階　平面図

求積表				
5.460	×	10.010	＝	54.6546
		計		54.6546
		１階床面積		54.65 ㎡
3.640	×	3.640	＝	13.2496
5.460	×	3.640	＝	19.8744
		計		33.1240
		２階床面積		33.12 ㎡
		延床面積		87.77 ㎡


1階外周長（基礎外周長）
（10.010＋5.460）×2=30.94m

図面名称	平面図	縮尺	1／100
調査年月日	平成２９年　４月１日		
請負者	株式会社　〇〇〇〇コンサルタント		
資格名称・作成者	補償業務管理士　・　中尾太郎　印		

様 式 第 9

整 理 番 号	1	図 面 番 号	2

所　在　地	東京都練馬区南大泉〇丁目〇番
所有者住所	東京都練馬区南大泉〇丁目〇番〇〇号
所　有　者	国　土　　二　郎

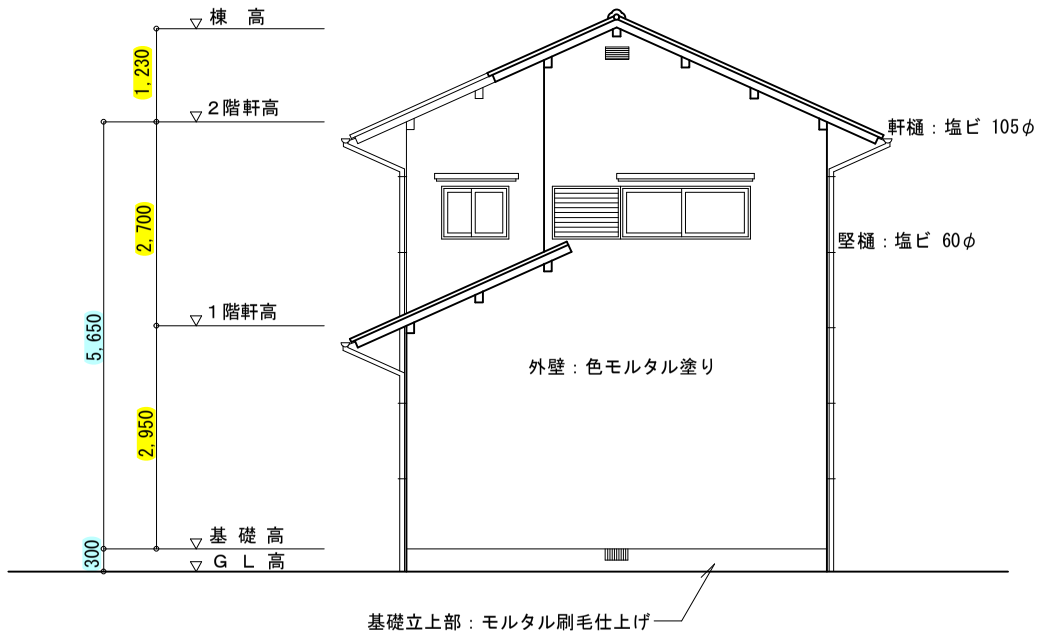

北　立 面 図



西　立 面 図


※H28年度から立面図は東西南北4面作成（標基建P44)

図 面 名 称	立　面　図	縮　尺	1／100
調 査 年 月 日	平成 29 年　4 月 1 日		
請　負　者	株式会社　〇〇〇〇コンサルタント		
資格名称・作成者	補償業務管理士 ・ 中 尾 太 郎　印		


様式第９

整理番号	1	図面番号	3

所在地	東京都練馬区南大泉〇丁目〇番
所有者住所	東京都練馬区南大泉〇丁目〇番〇〇号
所有者	国土　二郎

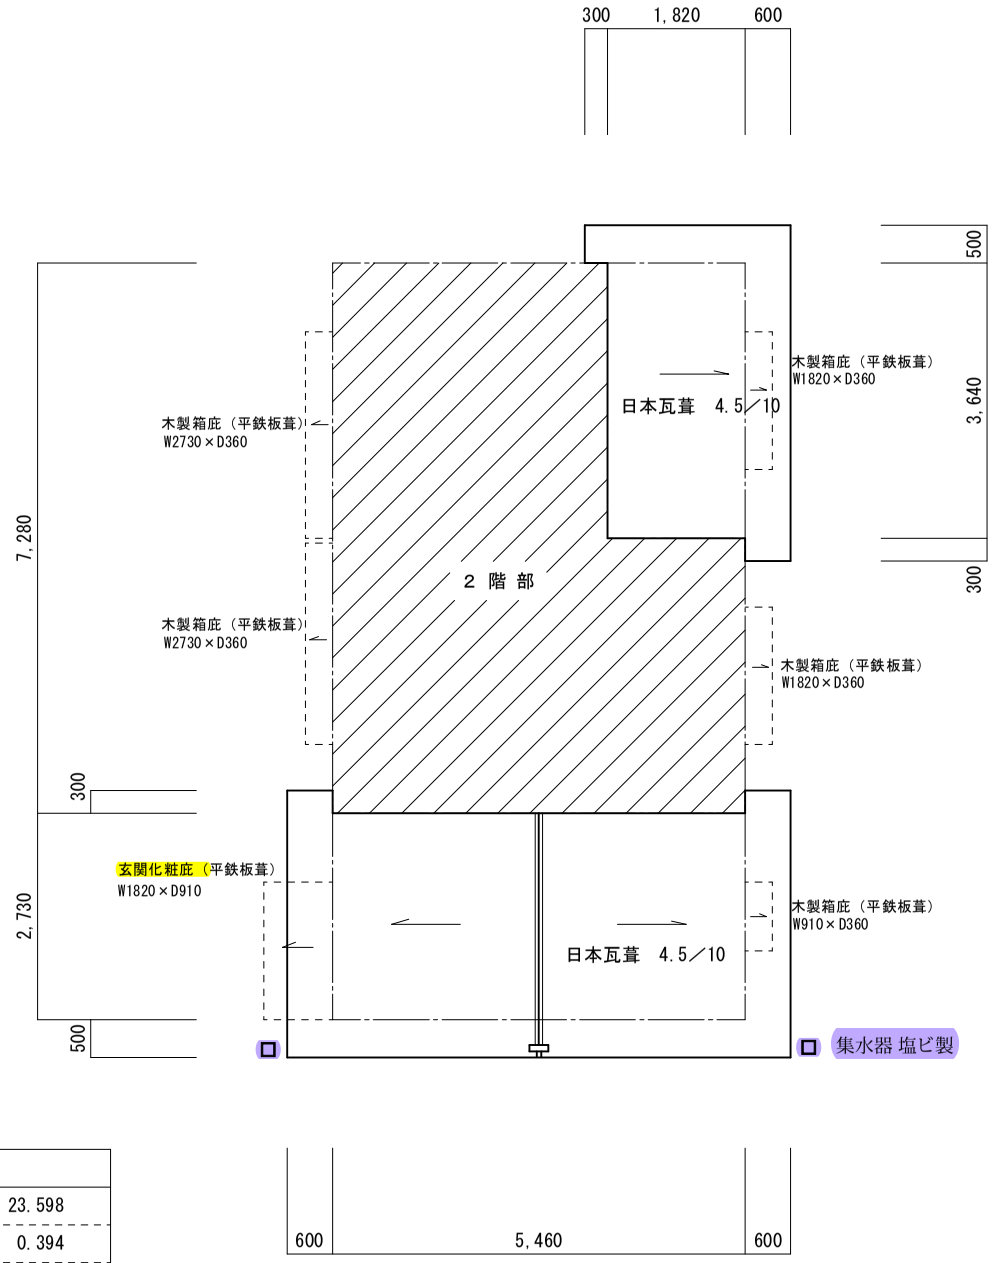

１階　屋根伏図

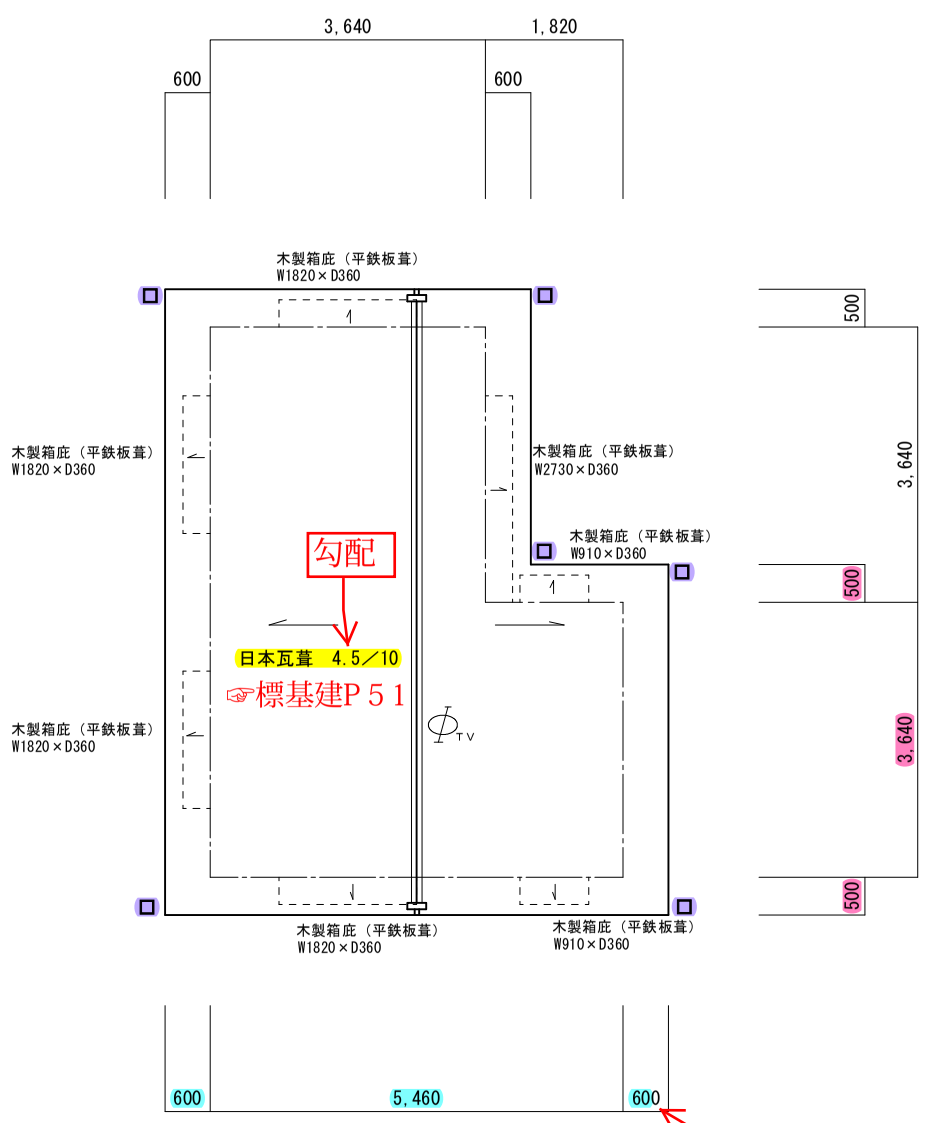

２階　屋根伏図

軒延長（呼樋）

求積表	☞標基建Ｐ５１			
6.660	× 3.230	× 1.097	＝	23.598
1.200	× 0.300	× 1.097	＝	0.394
4.140	× 2.420	× 1.097	＝	10.990
0.300	× 0.500	× 1.097	＝	0.164
0.600	× 0.300	× 1.097	＝	0.197
		計（１階）		35.343
6.660	× 4.640	× 1.097	＝	33.899
4.840	× 3.640	× 1.097	＝	19.326
		計（２階）		53.225
35.343 ㎡	＋ 53.225 ㎡		＝	88.568
		合　計		88.57 ㎡

伸び率

名称	規格	計算式	数量	単位
軒とい	φ105mm・塩ビ製・半円	3.64+4.64+8.28+3.53×2	23．62	m
立てとい	φ60mm・塩ビ製・丸型	6.55×6+3.85×2	47．00	m
集水器	φ105mm用・塩ビ製		8	ヶ所


立て樋
6.55＝
2階軒高5.650＋基礎高0.3＋呼樋（軒延長）0.6
※立て樋に呼樋の延長も加算
※軒高、基礎高は、立面図から

図面名称	屋根伏図	縮尺	1／100
調査年月日	平成２９年　４月１日		
請負者	株式会社　〇〇〇〇コンサルタント		
資格名称・作成者	補償業務管理士・中尾太郎　印		


様 式 第 9

整 理 番 号	1	図 面 番 号	4

所 在 地	東京都練馬区南大泉〇丁目〇番
所有者住所	東京都練馬区南大泉〇丁目〇番〇〇号
所 有 者	国 土 二 郎

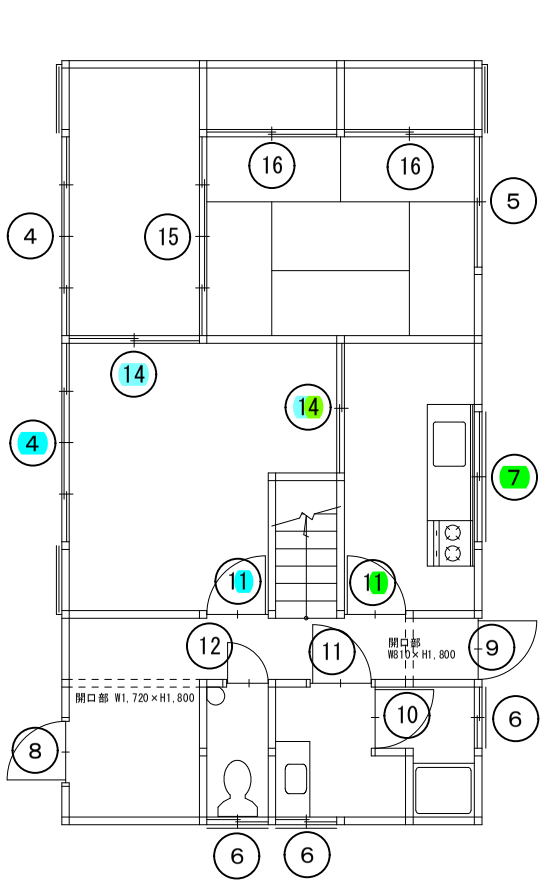

1 階　建具位置図

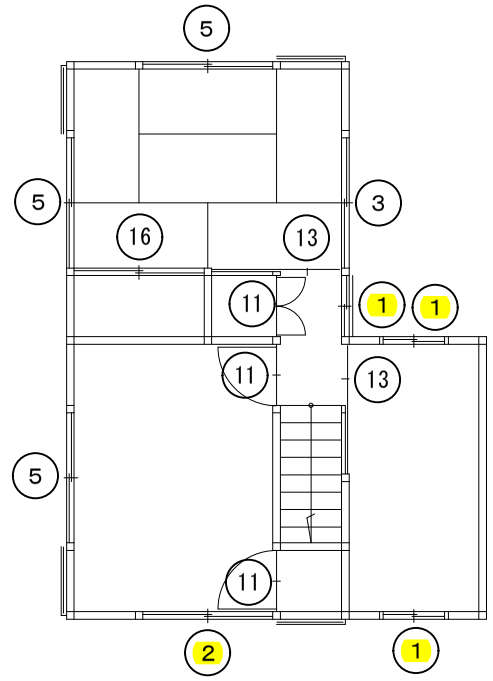

2 階　建具位置図

1カ所当たり開口部面積0.5㎡以下は、外壁・内壁面積から控除しない

建　具　表


	建具 No.	名　称	規 格 寸 法	ヶ所
金属製建具（サッシュ窓）	1	ｱﾙﾐｻｯｼｭ（雨戸無し）・〔ＡＢ〕	W 785 × H 604（0.474㎡・Ⅰ）	3
	2	ｱﾙﾐｻｯｼｭ（雨戸無し）・〔ＡＢ〕	W 1,692 × H 361（0.610㎡・Ⅰ）	1
	3	ｱﾙﾐｻｯｼｭ（雨戸無し）・〔ＡＢ〕	W 1,692 × H 604（1.021㎡・Ⅱ）	1
	4	ｱﾙﾐｻｯｼｭ（雨戸有り、鏡板有り）・〔ＡＣ〕	W 2,604 × H 1,788（4.655㎡・Ⅱ）	2
	5	ｱﾙﾐｻｯｼｭ（雨戸有り、鏡板有り）・〔ＡＣ〕	W 1,692 × H 604（1.021㎡・Ⅱ）	4
	6	ｱﾙﾐｻｯｼｭ（面格子付き）・〔ＡＥ〕	W 785 × H 604（0.474㎡・Ⅰ）	3
	7	ｱﾙﾐｻｯｼｭ（面格子付き）・〔ＡＥ〕	W 1,692 × H 604（1.021㎡・Ⅱ）	1
金属製建具（その他）	8	玄関アルミドアー	W 1,240 × H 2,210（2.740㎡）	1
	9	アルミドアー	W 786 × H 1,818（1.428㎡）	1
	10	アルミドアー	W 805 × H 1,818（1.463㎡）	1
木製建具	11	フラッシュ戸	W 805 × H 1,757（1.414㎡・Ⅰ）	6
	12	フラッシュ戸	W 645 × H 1,757（1.133㎡・Ⅰ）	1
	13	フスマ戸	W 805 × H 1,757（1.414㎡・Ⅰ）	2
	14	ガラス戸	W 1,715 × H 1,757（3.013㎡・Ⅰ）	2
	15	障　子	W 2,625 × H 1,757（4.612㎡・Ⅰ）	1
	16	フ ス マ	W 1,715 × H 1,757（3.013㎡・Ⅰ）	3

図 面 名 称	建 具 位 置 図	縮 尺	1／100
調 査 年 月 日	平成 29 年　4 月 1 日		
請 負 者	株式会社　〇〇〇〇コンサルタント		
資格名称・作成者	補償業務管理士 ・ 中 尾 太 郎　印		


様 式 第 9

整 理 番 号	1	図 面 番 号	5

所 在 地	東京都練馬区南大泉〇丁目〇番
所有者住所	東京都練馬区南大泉〇丁目〇番〇〇号
所 有 者	国 土 二 郎

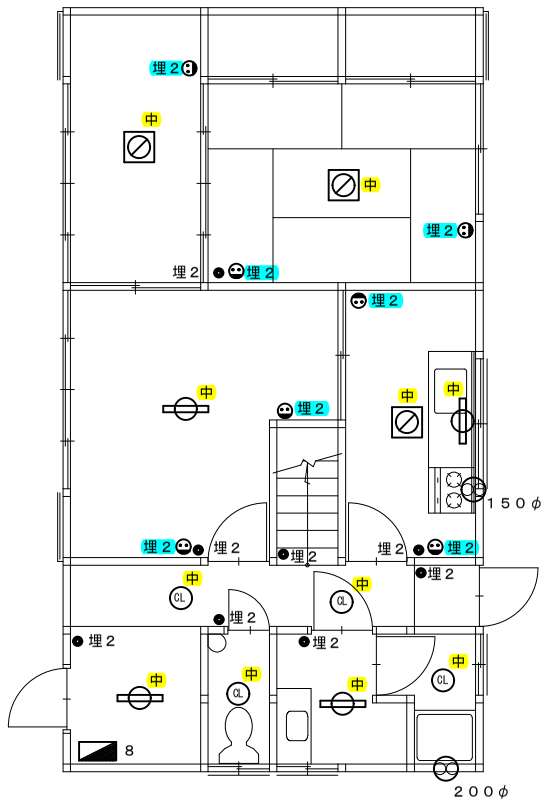

１階　設備位置図（電気設備）

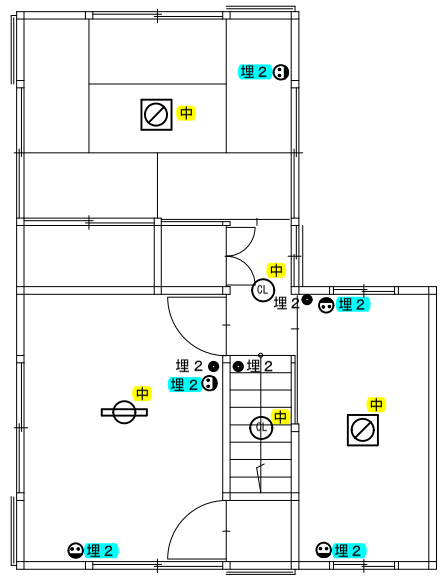

２階　設備位置図（電気設備）

☞標単建P43


電 気 設 備				
種 類	規格	１ 階	２ 階	計
照 明 設 備	中	１１	5	１６
コンセント	埋込・2口	7	5	１２
ス イ ッ チ	埋込・2連	8	3	１１
分 電 盤	ｺﾝﾊﾟｸﾄ型分岐ﾌﾞﾚｰｶ・8回路	1		1
合 計		２７	１３	４０
換 気 扇		2		2


図 面 名 称	設 備 位 置 図	縮 尺	1／１００
調 査 年 月 日	平成 ２９ 年 ４ 月 １ 日		
請 負 者	株式会社 〇〇〇〇コンサルタント		
資格名称・作成者	補償業務管理士 ・ 中 尾 太 郎 印		

様式第９

整理番号	1	図面番号	6

所在地	東京都練馬区南大泉〇丁目〇番
所有者住所	東京都練馬区南大泉〇丁目〇番〇〇号
所有者	国土　二郎

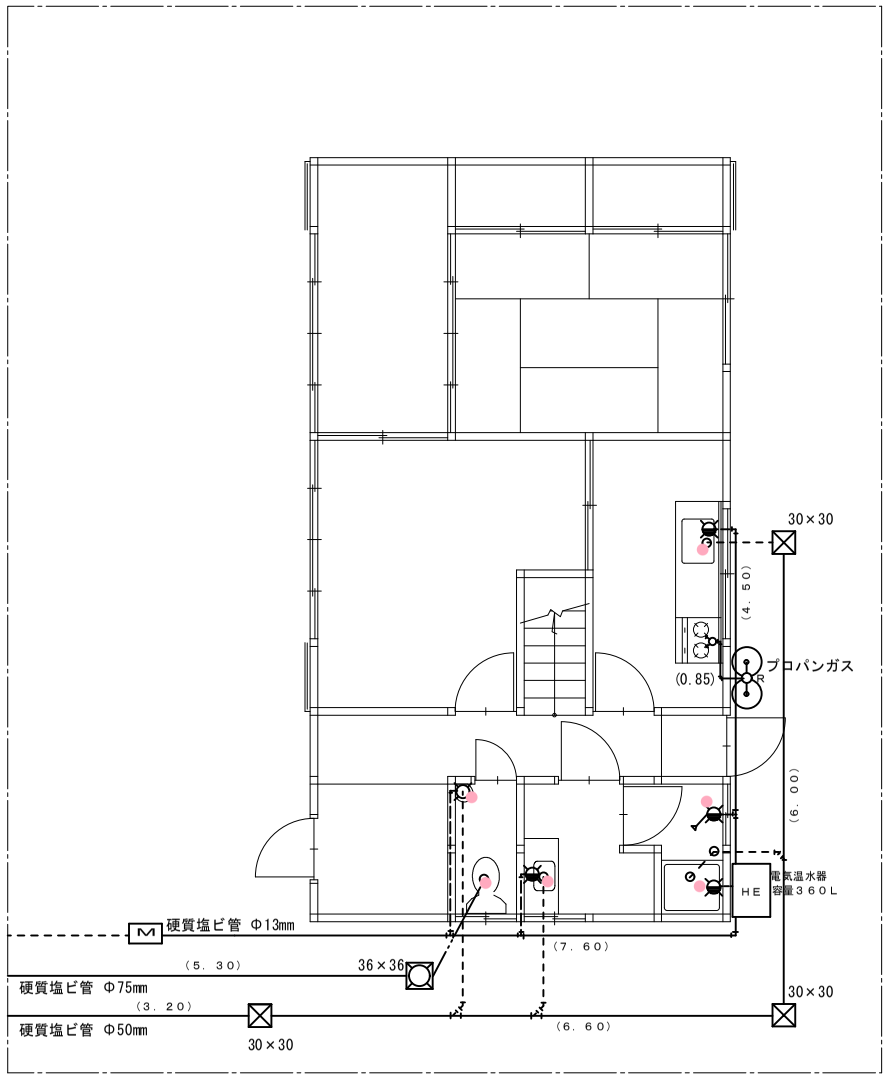

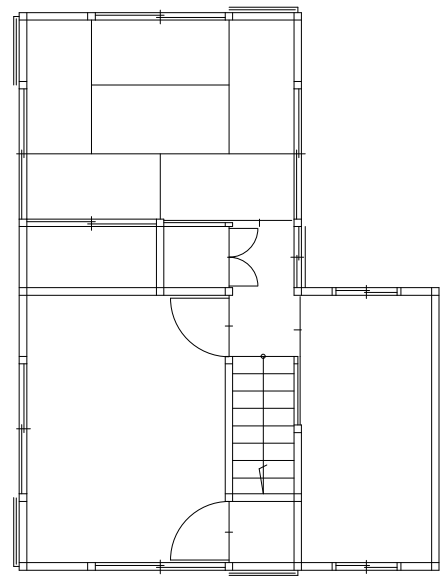

設備位置図（給水・排水・ガス設備）

☞標単建Ｐ５３

☞標単建Ｐ５５

水洗用便器についても屋内排水配管を１栓計上する。（H28改正）


ガス設備				
名称	形状寸法等	数量	単位	備考
ﾌﾟﾛﾊﾟﾝ設備	自動切替調整器、メーター付き	1	式	
ガス栓	２口カラン	1	ヶ所	
ガス管	１５Ａ	0.85	m	
給水・給湯設備				
混合水栓	φ１３mm用	2	栓	
ｼｬﾜｰ付混合水栓	φ１３mm用	1	栓	
屋内給水配管	硬質塩ビ管・φ１３mm	6	栓	
屋外給水配管	硬質塩ビ管・φ１３mm	12.10	m	7.60+4.50
電気温水器	貯湯容量３６０Ｌ	1	基	
排水設備				
屋内排水配管	硬質塩ビ管・φ５０mm	5	栓	
屋外排水配管	硬質塩ビ管・φ５０mm	15.80	m	3.20+6.60+6.00
屋内排水配管	硬質塩ビ管・φ７５mm	1	栓	
屋外排水配管	硬質塩ビ管・φ７５mm	5.30	m	
溜ます（雑排水用）	内法　３０×３０	3	ヶ所	
汚水兼用ます	内法　３６×３６	1	ヶ所	


図面名称	設備位置図	縮尺	1／１００
調査年月日	平成２９年　４月１日		
請負者	株式会社　〇〇〇〇コンサルタント		
資格名称・作成者	補償業務管理士・中尾太郎　印		

様 式 第 9

整 理 番 号	1	図 面 番 号	7

所 在 地	東京都練馬区南大泉〇丁目〇番
所有者住所	東京都練馬区南大泉〇丁目〇番〇〇号
所 有 者	国 土 二 郎

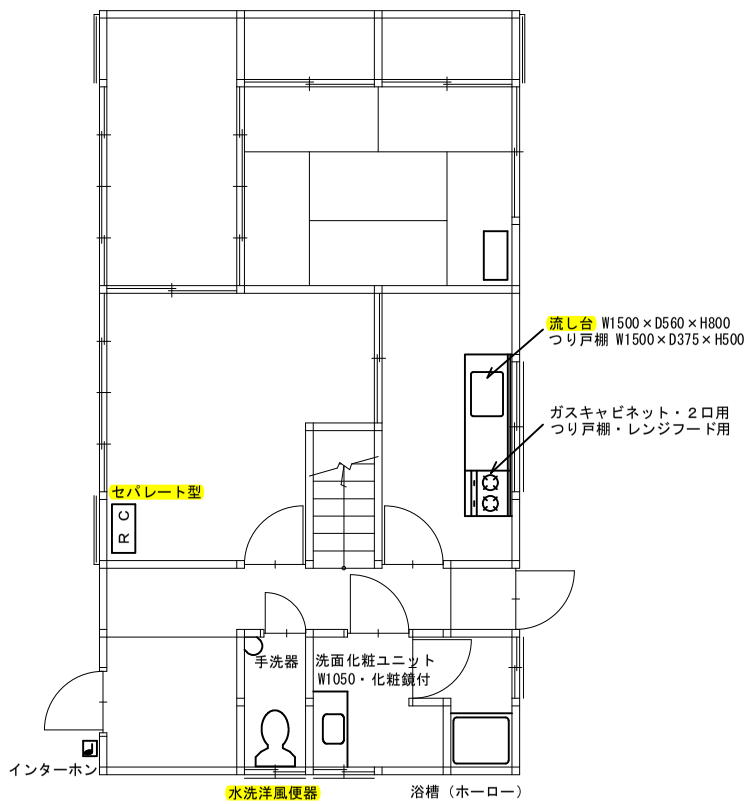

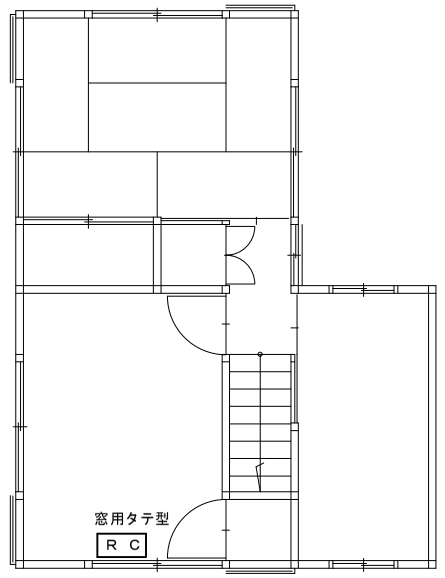


設備位置図（衛生・空調設備等）

図 面 名 称	設 備 位 置 図	縮 尺	1／100
調 査 年 月 日	平成 29 年 4 月 1 日		
請 負 者	株式会社 〇〇〇〇コンサルタント		
資格名称・作成者	補償業務管理士 ・ 中 尾 太 郎 印		

建　物　調　査　書

整理番号	1	図面番号	8

所　在　地	東京都練馬区南大泉〇丁目〇番
所有者住所	東京都練馬区南大泉〇丁目〇番〇〇号
所　有　者	国　土　　二　郎

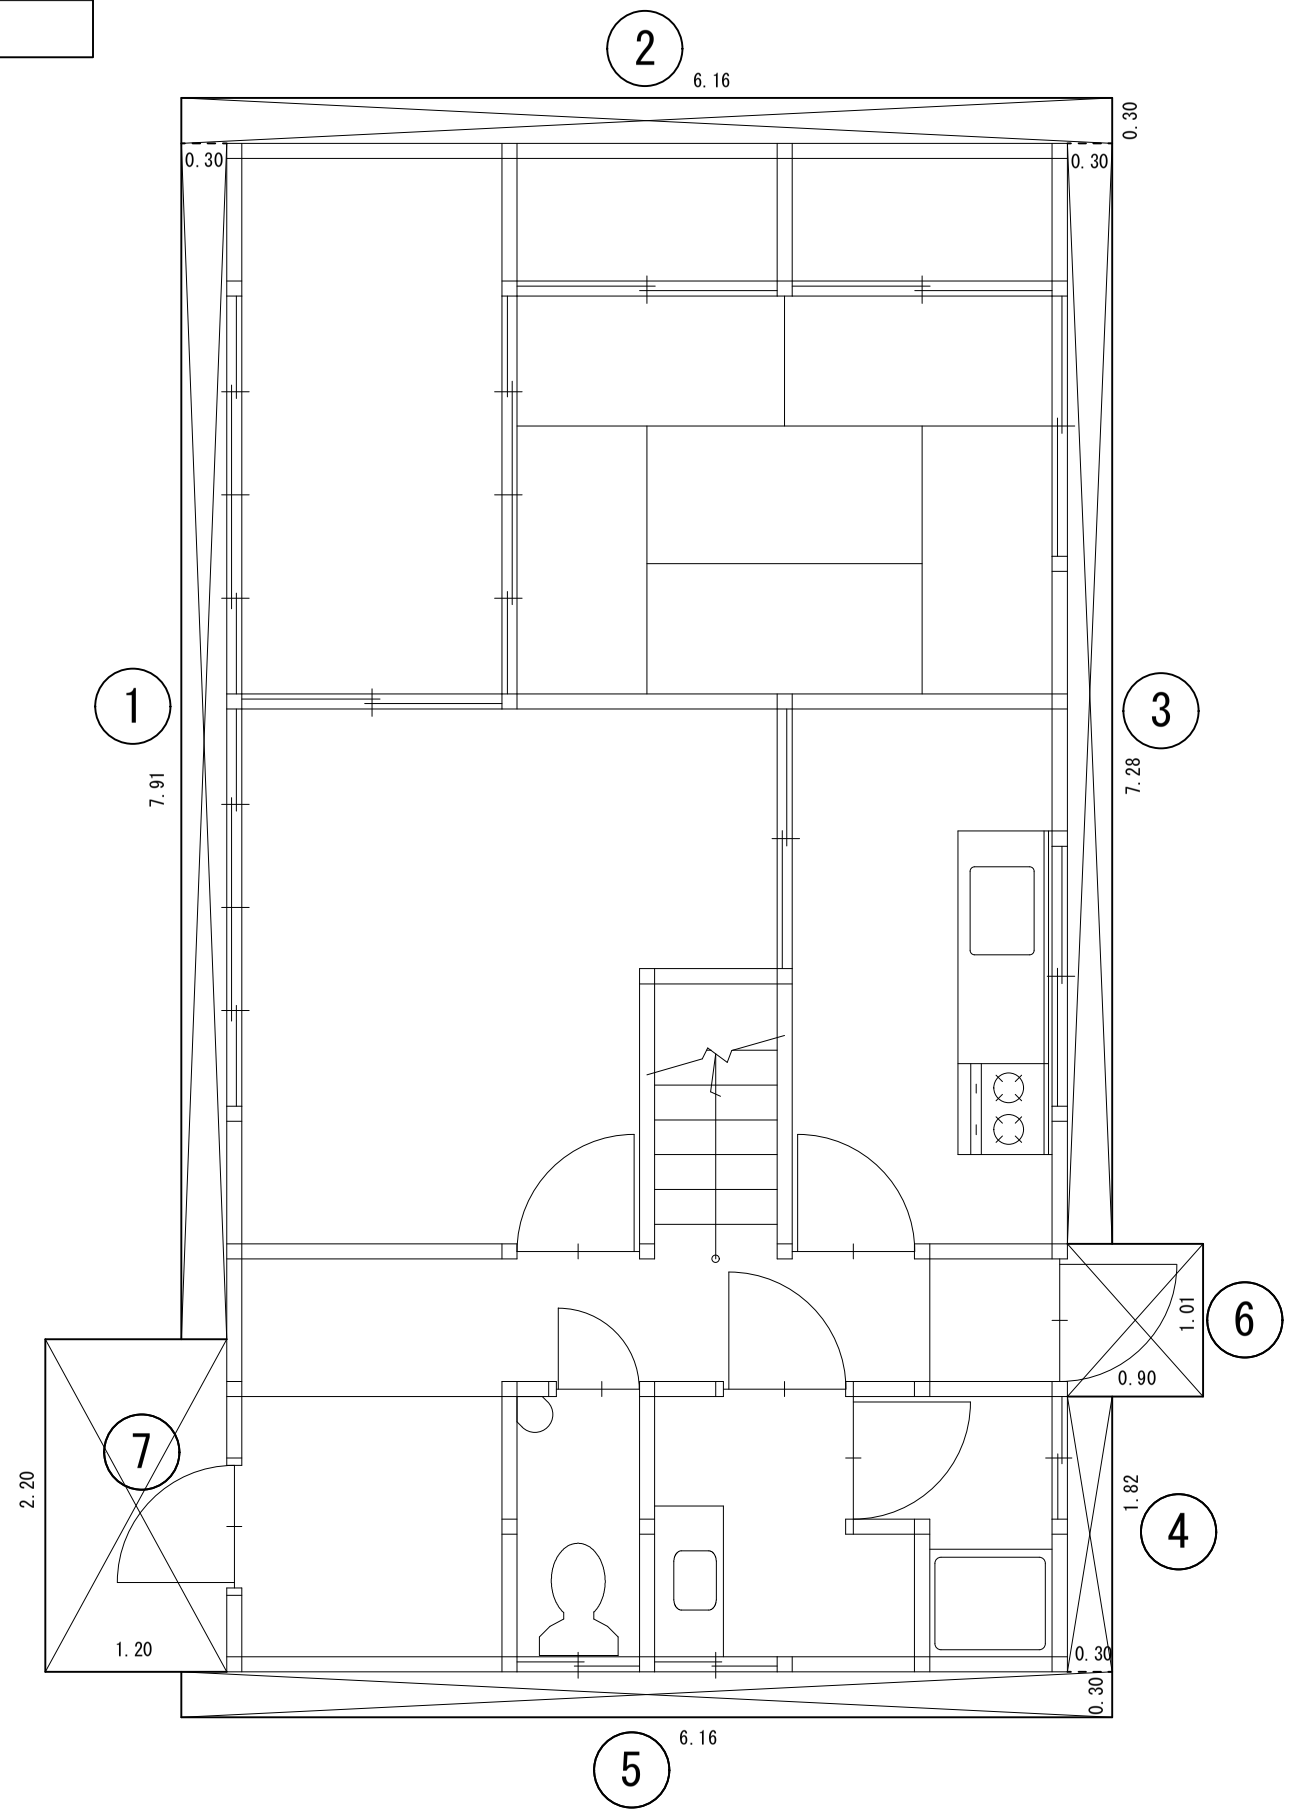

土間コンクリート叩き　厚１２０

玄　関	１．８２	× １．８２	＝	３．３１２４
便　所	１．８２	× ０．９１	＝	１．６５６２
浴　室	１．８２	× ０．９１	＝	１．６５６２
	０．４５	× ０．９１	＝	０．４０９５
勝手口	０．９１	× ０．９１	＝	０．８２８１
				７．８６ ㎡

土間コンクリート叩き　厚９０　モルタル塗

１	７．９１	× ０．３０	＝	２．３７３０
２	６．１６	× ０．３０	＝	１．８４８０
３	７．２８	× ０．３０	＝	２．１８４０
４	１．８２	× ０．３０	＝	０．５４６０
５	６．１６	× ０．３０	＝	１．８４８０
６	０．９１	× １．０１	＝	０．９０９０
				９．７１ ㎡

土間コンクリート叩き　厚１５０

７	２．２０	× １．２０	＝	２．６４００
				２．６４ ㎡

土間コンクリート叩き厚９０内訳
〔２〕基礎工事費
　６ 勝手口　0.9090→0.91㎡
〔14〕建物附随工作物工事費
　１～５計　8.799→8.80㎡

図面名称	土間コン求積図	縮　尺	１／５０
調査年月日	平成 ２９年　４ 月 １ 日		
請　負　者	株式会社　〇〇〇〇コンサルタント		
資格名称・作成者	補償業務管理士 ・ 中 尾 太 郎　印		