
整理番号	1	図面番号	1

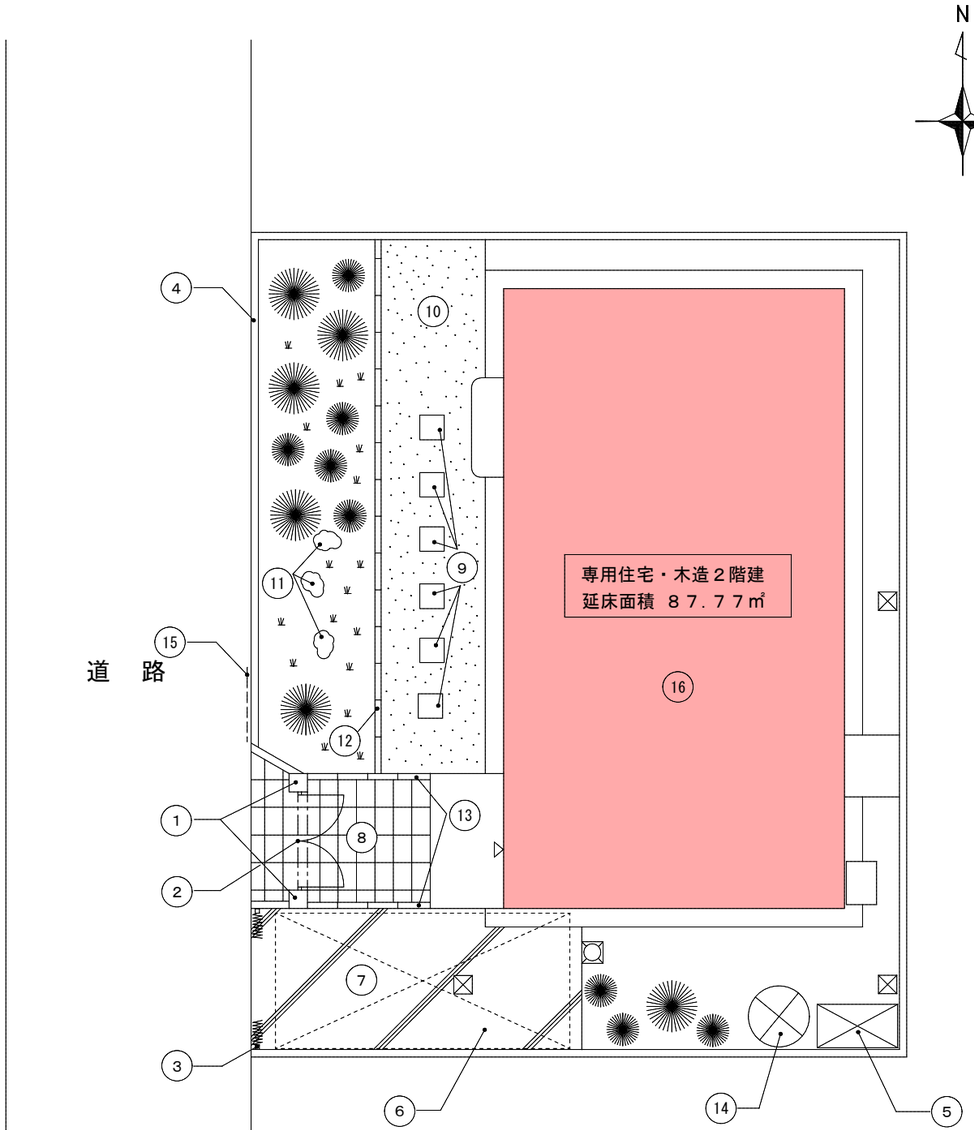

附帯工作物リスト

番号	種　類	構造・形状・寸法	数量	単位	備　考
①	ブロック積角門柱	ｺﾝｸﾘｰﾄﾌﾞﾛｯｸ造 ７段積・300㎜角・高さ200㎜	2	ヶ所	
②	アルミ形材両開門扉	ｱﾙﾐ製・幅1600㎜・高さ1400㎜・直付	1	ヶ所	
③	アルミ伸縮門扉(両引)	ｱﾙﾐ製・幅5100㎜・高さ1150㎜	1	ヶ所	
④	擬石ブロック積塀	擬石ﾌﾞﾛｯｸ造・６段積・厚150㎜	44.65	m	
⑤	組立物置	鋼製・1320㎜×710㎜・H1620㎜	1	ヶ所	
⑥	アルミ片流れカーポート	ｱﾙﾐ製・片持支柱・4802㎜×2407㎜	1	ヶ所	
⑦	土間コンクリート叩き	ｺﾝｸﾘｰﾄ造・厚120㎜・無筋	11.94	㎡	
⑧	御影石敷き	石造・450㎜×300㎜×30㎜	5.88	㎡	
⑨	コンクリート平板敷き	ｺﾝｸﾘｰﾄ製・400㎜×400㎜×60㎜	0.96	㎡	
⑩	砂利敷き	砂利・厚90㎜	13.50	㎡	
⑪	庭　石	庭石・400㎜×300㎜×300㎜	3	個	
⑫	ブロック縁石	ｺﾝｸﾘｰﾄﾌﾞﾛｯｸ造・120㎜×120㎜×600㎜	8.71	m	
⑬	擬石ブロック縁石	擬石ﾌﾞﾛｯｸ造・498㎜×190㎜×120㎜	4.00	m	
⑭	掘井戸	掘井戸・内径750㎜×深10m・井戸側付	1	ヶ所	
⑮	亜鉛鉄板平看板	木製・900㎜×1800㎜	1	ヶ所	
⑯	電話設備	１回線１台	1	式	

図面名称	附帯工作物配置図	縮尺	1／100
調査年月日	平成２９年　４月１日		
請負者	株式会社　○○○○コンサルタント		
資格名称・作成者	補償業務管理士　・　中尾　太郎　印		